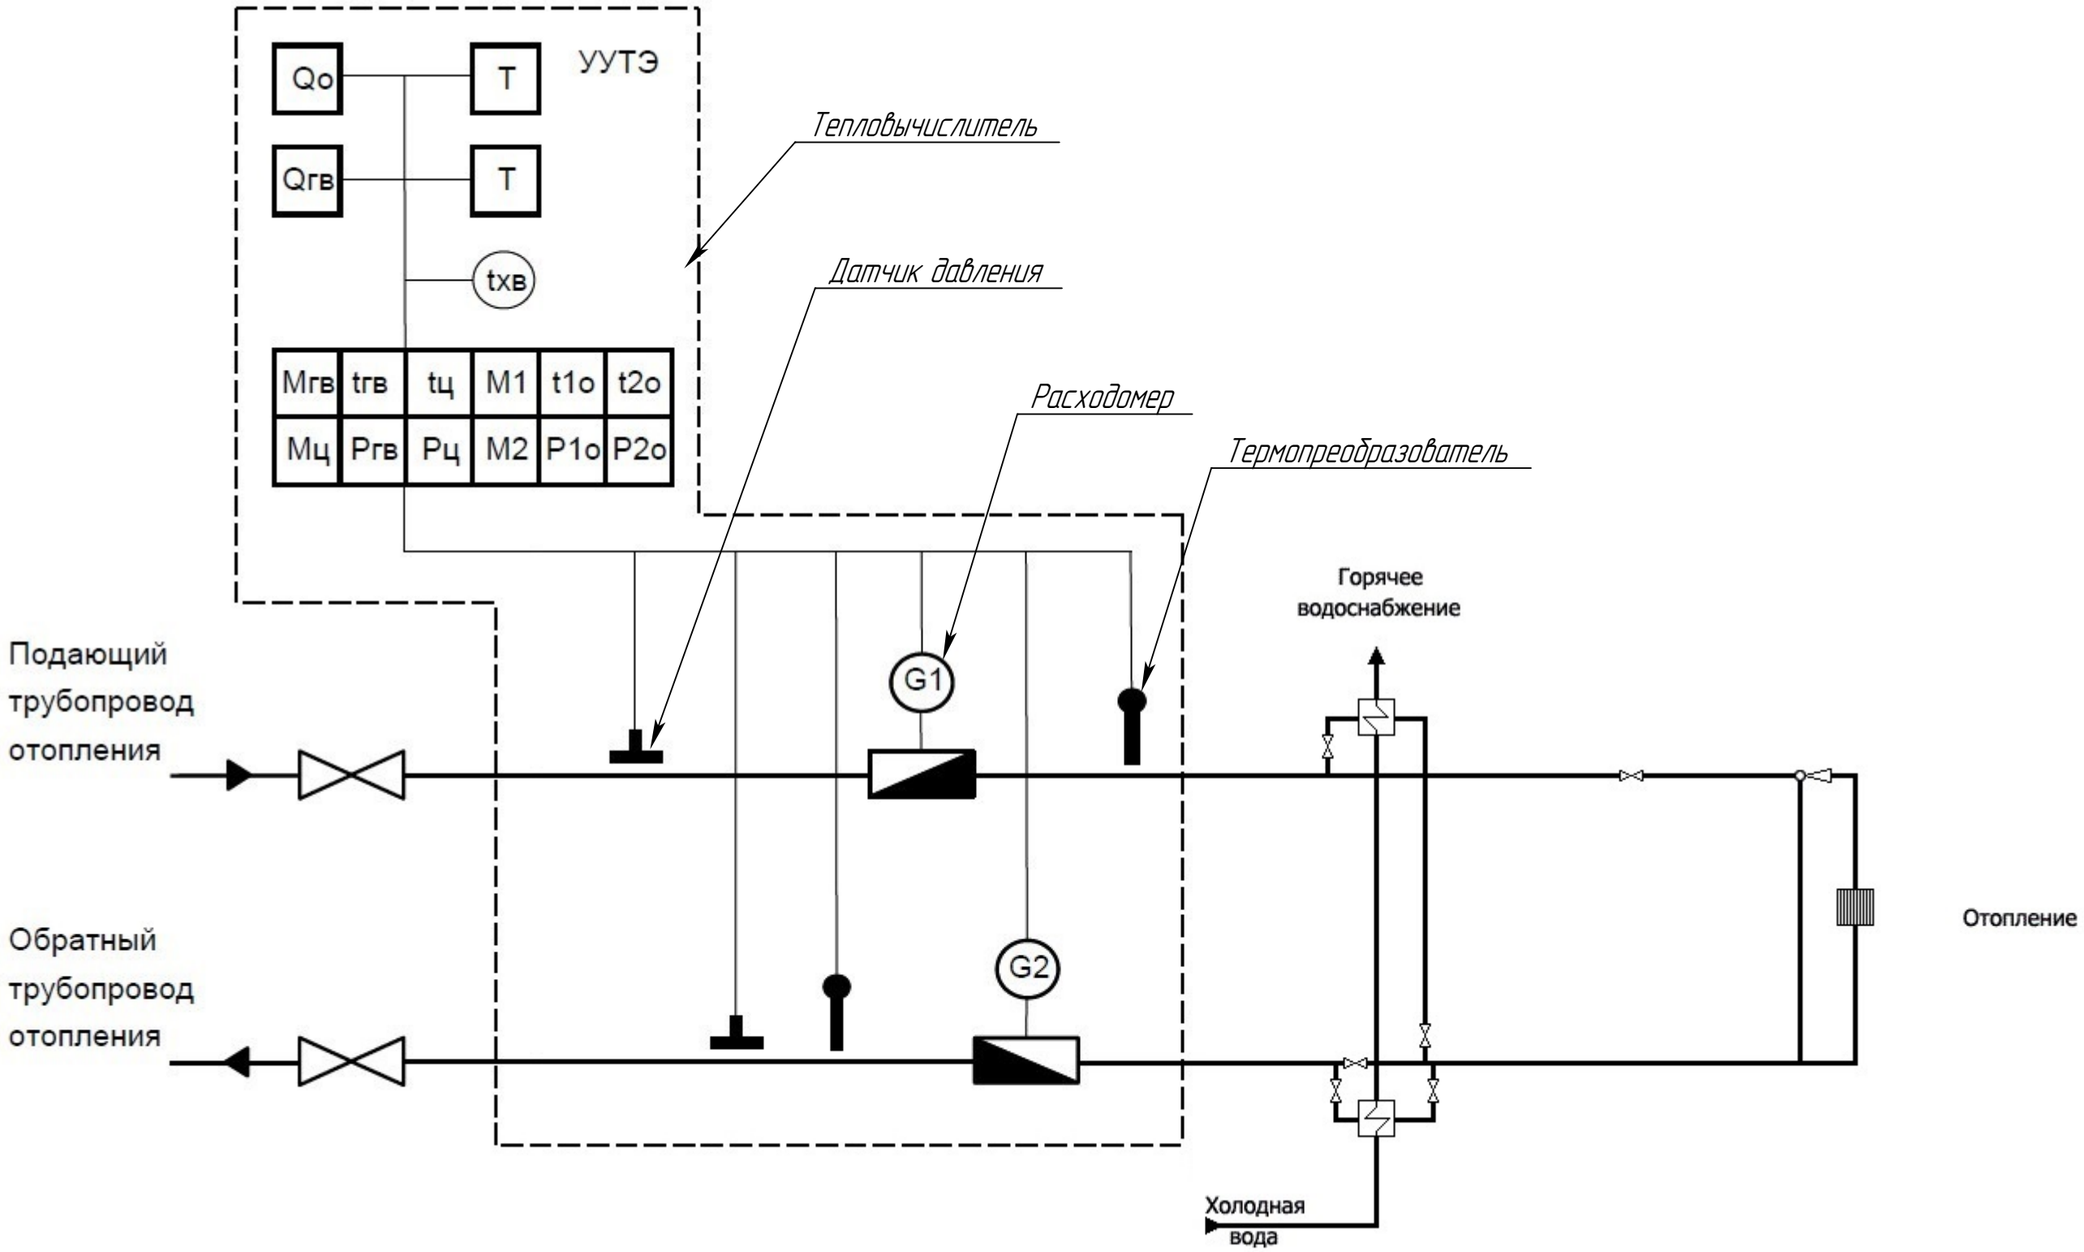

Изм.	Кол.уч.	Лист	№ докум.	Подп.	Дата	54-000/02-2026-УУТЭ		
						МКЖД Амурская обл., г.Благовещенск, ул. Текстильная, д. 33/1		
ГИП		Горбунов				Узел учета тепловой энергии	Стадия	Лист	Листов
Нач.отд.		Горбунов					Р	9	23
Исполн.		Мелкумян							
Н. контр.						Схема функциональная	ООО "С-ХОЛДИНГ"		

Перв. примен.

Справ. №

Подп. и дата

Инв.№ дубл.

Взам.инв.№

Подп. и дата

Инв.№ подл.

Копировал

Формат А3